LEGENDA

PAREDES À CONSTRUIR

PAREDES À MANTER

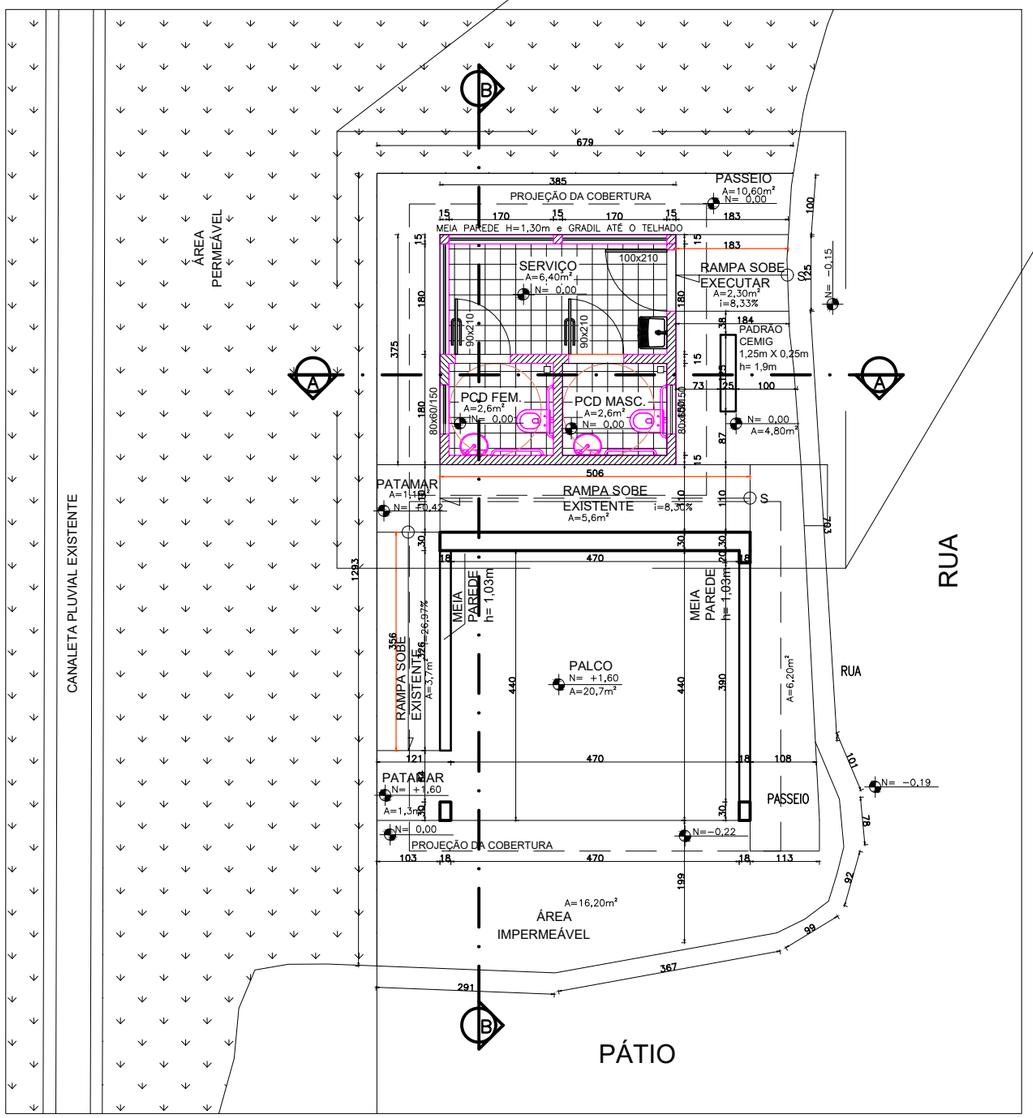

1 PLANTA SANITÁRIOS
ESCALA 1:100

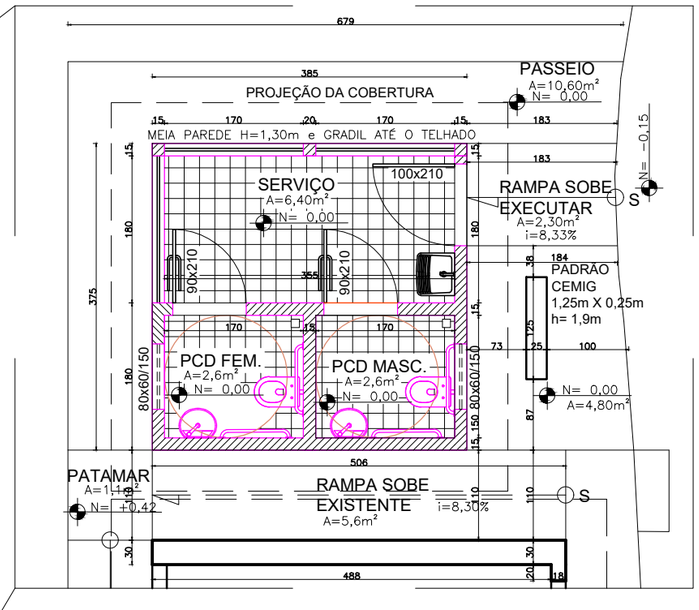

2 PLANTA SANITÁRIOS
ESCALA 1:75

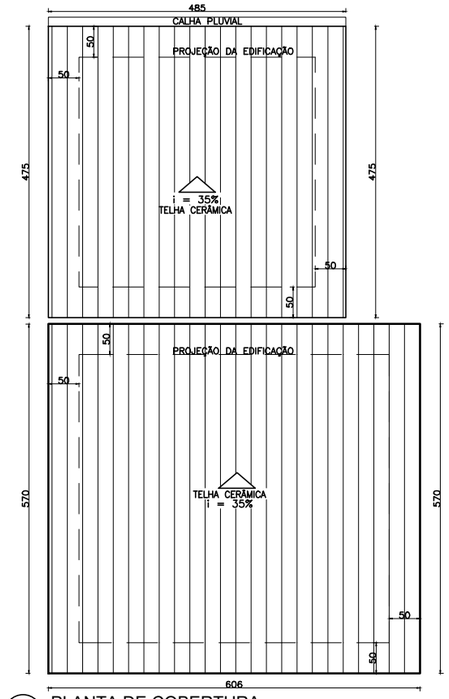

3 PLANTA DE COBERTURA
ESCALA 1:100

4 PLANTA DE LOCALIZAÇÃO
SEM ESCALA

	PREFEITURA MUNICIPAL DE MARIANA	
	Título: Projeto Básico Sanitários	Desenho data: 02.07.2024
Secretário de Obras:	Conteúdo: Planta,Cobertura e Localização	Escala: Indicada
Leonardo Rodrigues Santos	Departamento/Setor: Secretaria de Obras e Desenvolvimento Urbano	Desenho: Luciene venâncio/ Helen
	Local: Rua Diamantina,368- Bairro Cabanas	Folha Nº: 01/02