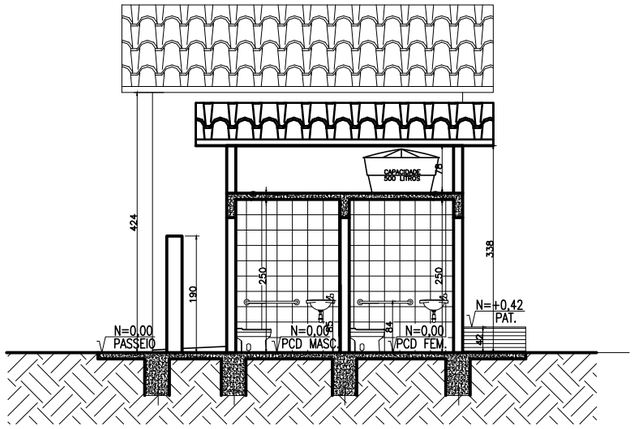

1 CORTE A-A
ESCALA 1:75

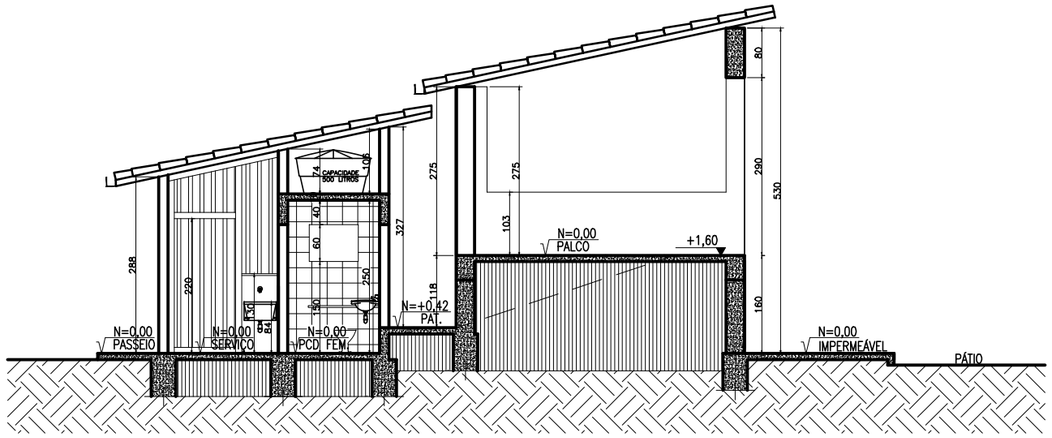

2 CORTE B-B
ESCALA 1:75

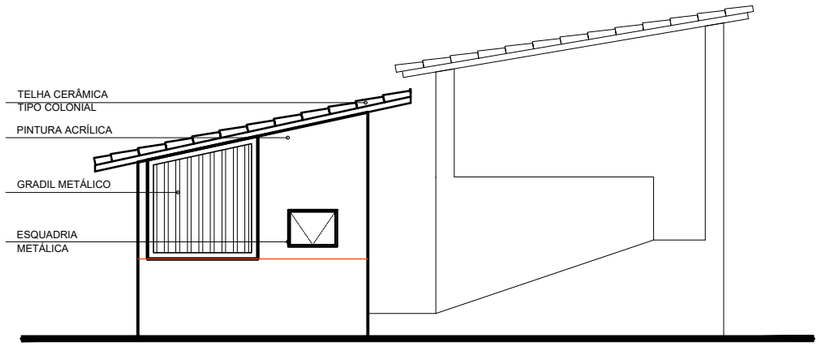

3 ELEVAÇÃO LATERAL ESQUERDA
ESCALA 1:75

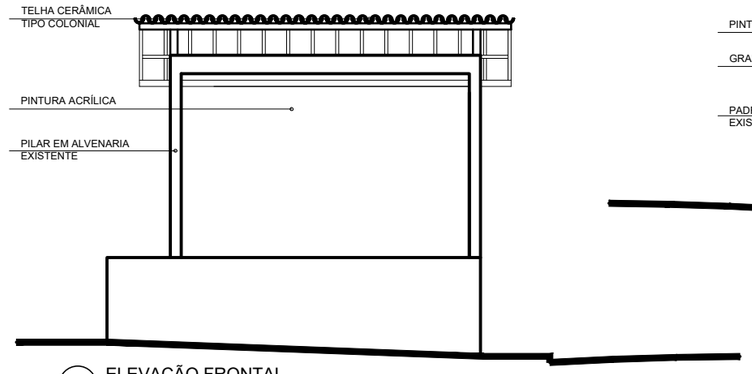

4 ELEVAÇÃO FRONTAL
ESCALA 1:75

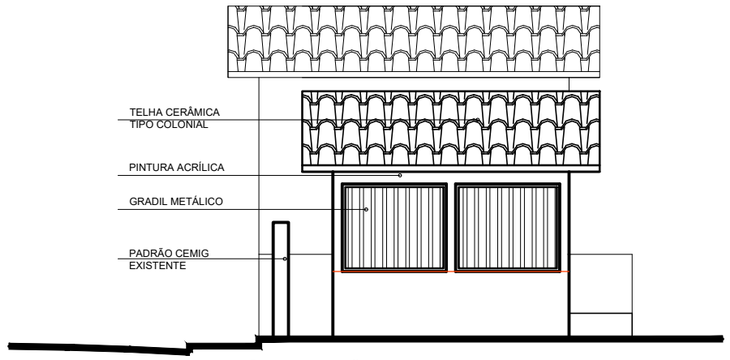

5 ELEVAÇÃO POSTERIOR
ESCALA 1:75

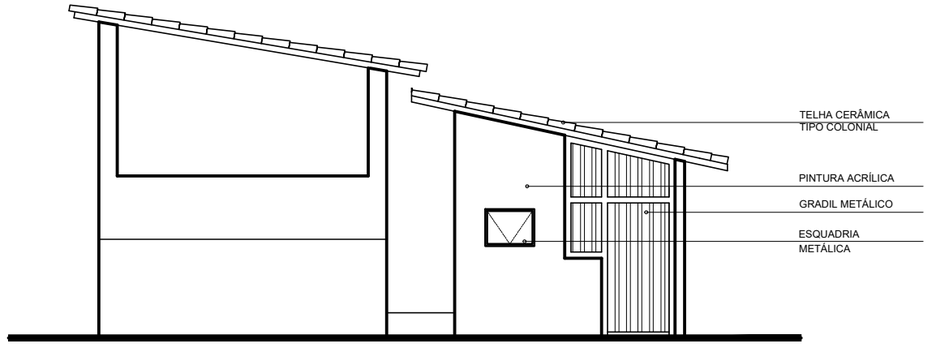

6 ELEVAÇÃO LATERAL DIREITA
ESCALA 1:75

	PREFEITURA MUNICIPAL DE MARIANA	
	Título: Projeto Básico Sanitários	Desenho data: 02.07.2024
Secretário de Obras:	Conteúdo: Cortes e Elevações	Escala: Indicada
Leonardo Rodrigues Santos	Departamento/Setor: Secretaria de Obras e Desenvolvimento Urbano	Desenho: Luciene venâncio/ Helen
	Local: Rua Diamantina,368- Bairro Cabanas	Folha Nº: 02/02